LINE NO.	SERVICE	NPS	CLASS	MATERIAL	DESIGN PRESS	DESIGN TEMP	FLANGE CLASS
8"-FG-1700-B3S	FG	8	B3S	A312 TP304L	520 PSIG	-270 / 140 F	CL300 RF

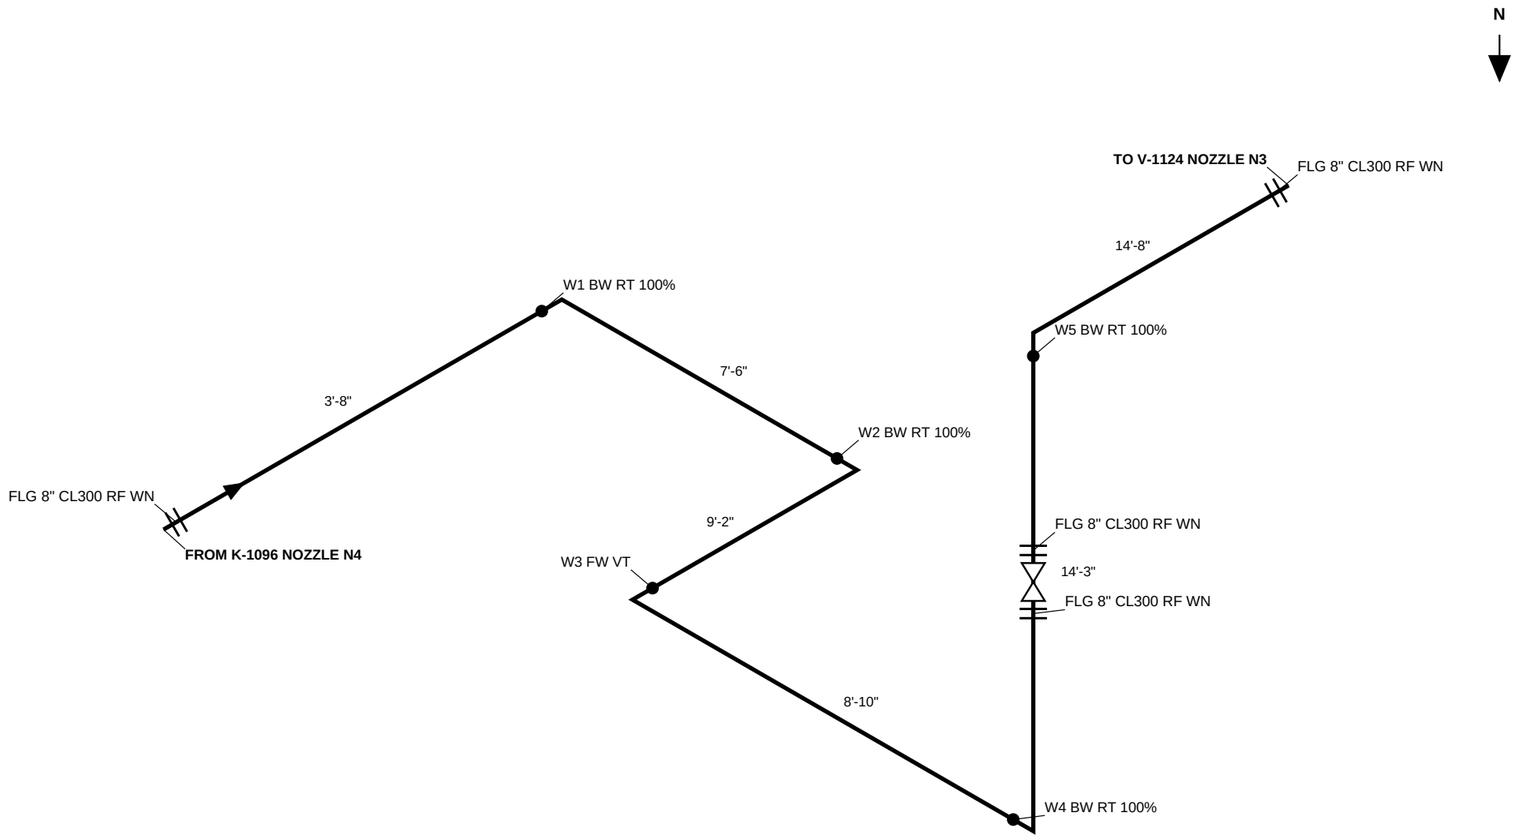

GENERAL NOTES

1. ALL DIMENSIONS ARE IN FEET AND INCHES. ISOMETRIC IS NOT TO SCALE.
2. PIPING CLASS, MATERIAL AND DESIGN CONDITIONS ARE AS SHOWN IN THE LINE DATA TABLE.
3. FLANGES PER ASME B16.5. FLANGE CLASS SHALL BE RATED FOR THE DESIGN PRESSURE (SEE FLANGE RATING REFERENCE): CL300 FOR THIS LINE.
4. WELDING AND EXAMINATION PER ASME B31.3 PARA. 341. CLASS B3S IS COLD SERVICE: FULL-PENETRATION BUTT WELDS (BW) WITH 100% RT. SOCKET AND FILLET WELDS ARE NOT PERMITTED.
5. WELDS ARE IDENTIFIED IN THE WELD TABLE AS SHOP OR FIELD. NOZZLE ORIENTATIONS PER EQUIPMENT DRAWINGS.
6. PIPE SUPPORTS ARE BY OTHERS. SUPPORT LOCATIONS PER STRESS ANALYSIS.

REFERENCE CODES AND STANDARDS

- ASME B31.3 PROCESS PIPING
- ASME B16.5 PIPE FLANGES AND FLANGED FITTINGS
- ASME B16.9 FACTORY-MADE BUTT-WELDING FITTINGS

BILL OF MATERIALS

ITEM	QTY	DESCRIPTION
1	21 FT	PIPE 8" SCH 40S SMLS, A312 TP304L
2	5	ELBOW 90 DEG LR 8" BW, A403 WP304L
3	4	FLANGE WN 8" CL300 RF, A182 F304L
4	2	GASKET SPIRAL WOUND 8" CL300
5	1	GATE VALVE 8" CL300 FLG, BODY CF3M

WELD TABLE

WELD NO.	TYPE	NPS	EXAMINATION	SHOP / FIELD
W1	BW	8	RT 100%	FIELD
W2	BW	8	RT 100%	SHOP
W3	FW	8	VT	FIELD
W4	BW	8	RT 100%	FIELD
W5	BW	8	RT 100%	FIELD

FLANGE RATING REFERENCE

ASME B16.5, SS GROUP 2.1, AT 100 F

FLANGE CLASS	MAX ALLOWABLE PRESSURE
CLASS 150	275 PSIG
CLASS 300	720 PSIG
CLASS 600	1440 PSIG
CLASS 900	2160 PSIG
CLASS 1500	3600 PSIG

REV	DATE	DESCRIPTION	BY	CHK
A	2025-11-18	ISSUED FOR REVIEW	KC	KR
B	2025-12-21	ISSUED FOR DESIGN	JB	MS
C	2026-03-29	REVISED PER CLIENT COMMENTS	JC	HB
D	2026-04-20	ISSUED FOR APPROVAL	GM	AD

PROJECT
BLUE RIDGE LNG TERMINAL - PHASE 2

TITLE
PIPING ISOMETRIC
LINE 8"-FG-1700-B3S - TRAIN 3

DRAWING NUMBER	REV
BRL-PIP-ISO-0664	**D**

SCALE	SHEET	DATE	DISCIPLINE
NTS	**1 OF 1**	**2026-04-20**	**PIPING**

DRAWN BY	CHECKED BY	APPROVED BY
K. JACOBSON	**T. KRAMER**	**J. LOVE**